

Detailplan erstellen

Name:

Datum:

Lernziele Modul

- Sie benennen die relevanten Anforderungen an die Apparatemontage (z.B. bauliche Voraussetzungen, Schallschutz). Ja ☐ Nein ☐
- Sie bestimmen anhand von Beispielen den Platzbedarf, Achsabstände und Montagehöhen von Apparaten und den zugehörigen Garnituren. Ja ☐ Nein ☐
- Sie kennen die relevanten Achsmasse, Abstände und Montagehöhen der wichtigsten sanitären Apparate. Ja ☐ Nein ☐

Lernprodukte

- Leistungsnachweis «Detailplanung Badezimmer» ☐

Situation

Als Sanitärinstallateur erhalten Sie nicht immer fertige Badezimmerpläne. Es ist auch Ihre Aufgabe mit der Apparateauswahl des Kunden und den vorhandenen Platzverhältnissen das Badezimmer optimal einzuteilen und den Kunden zu beraten.


Als Hilfsmittel verwenden Sie Massskizzen von Lieferanten und Planungshilfen. Nachträgliche Anpassungen sind sehr kostenintensiv, da auf den Wänden bereits Platten verlegt wurden. Damit der Kunde von seinem neuen Bad nicht enttäuscht ist, gibt es gewisse Grundregeln und Masse, die eingehalten werden sollen.

Zu jedem Apparat gibt es gewissen Grundregeln und die sollen Sie als Fachmann nun zuerst lernen. In diesem Auftrag sollen Sie die Grundlagen der Badplanung lernen. Gehen wir es an...



Auftrag 1

1. Gehen Sie in die WC Anlagen im Schulhaus und notieren Sie die in den Nasszellen vorhandenen Apparate und Garnituren. Achten Sie darauf, dass Sie keinen Apparat oder ein Bauteil vergessen, welcher durch den Sanitärinstallateur geliefert und montiert wird.

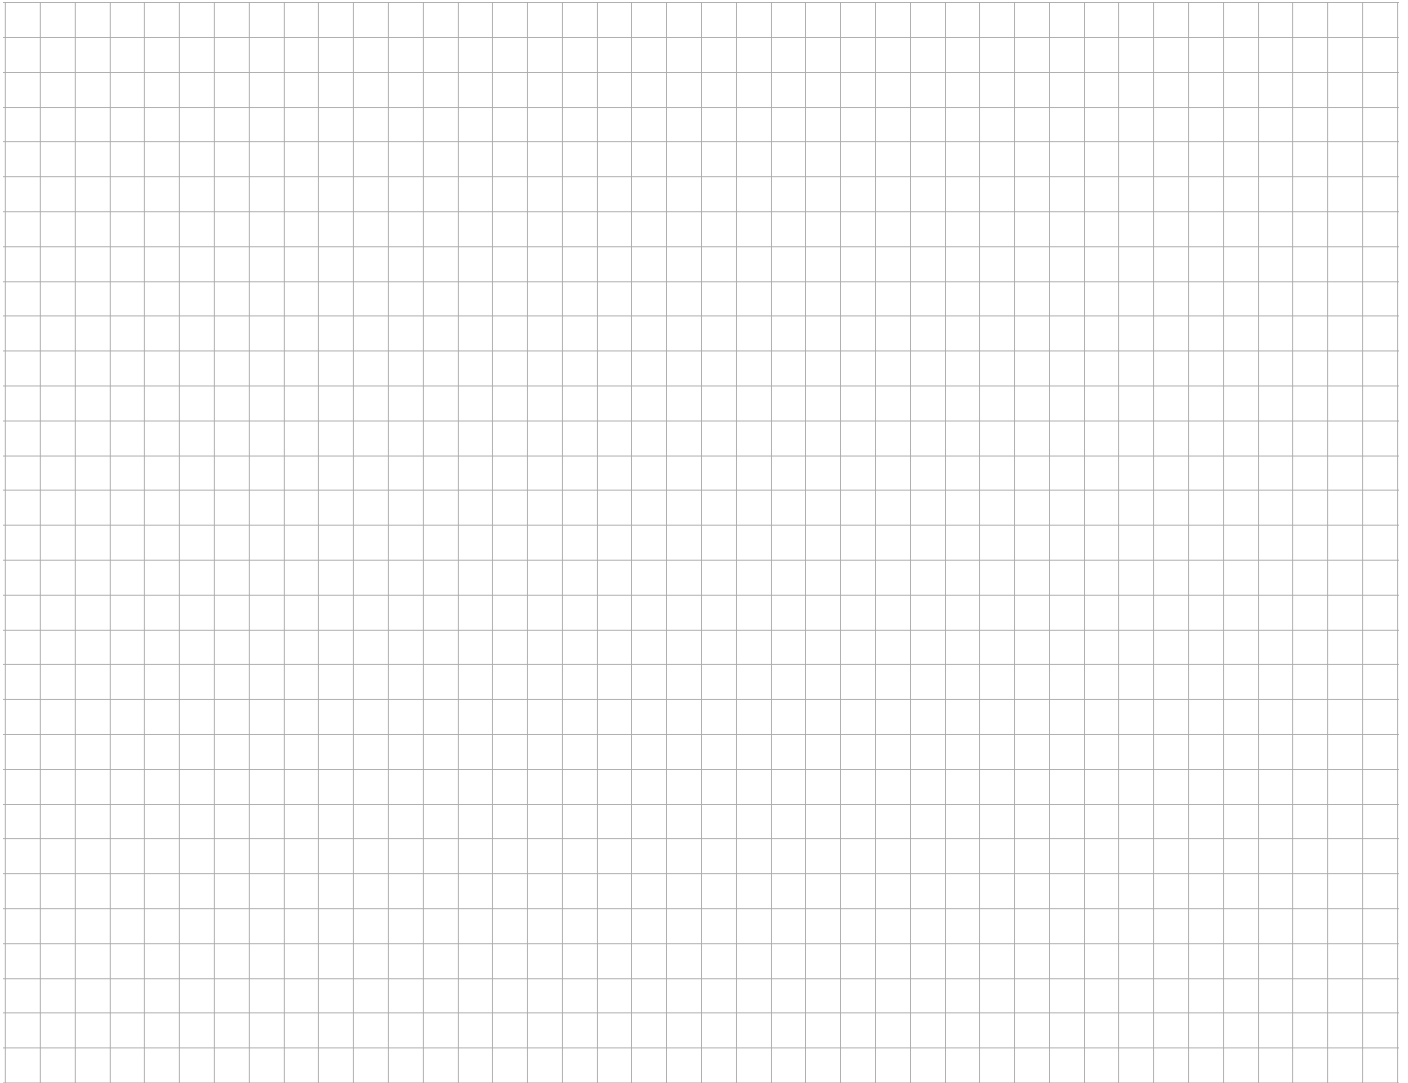

2. Haben Sie auf der Baustelle schon mal Probleme erlebt, bei welchen Apparate und oder Garnituren falsch eingeteilt wurden? Notieren Sie die Situationen und diskutieren Sie es mit dem Banknachbar.



Nachfolgend sehen Sie eine Übersicht der wichtigsten Apparate und deren Montagehöhen. Studieren Sie die Übersicht und zeichnen Sie nachfolgend die wichtigsten Apparate und deren Masse im Massstab 1:20 auf.

[Link zum Dokument](#)

Unter nachfolgendem Link finden Sie die Übersicht der Apparate



Diese Masse dienen nur der groben Übersicht. Es gibt heute tausende verschiedene Apparate für alle erdenklichen Situationen und Ansprüche. Als Sanitärinstallateur erhalten Sie von Apparate - Grosshandel Listen mit den Apparaten, welche vom Kunden ausgelesen wurden. In dieser Apparatelite finden Sie die [Artikelnummer](#) jedes Bauteils. Über diese Artikelnummer können Sie Detailpläne und Angaben herausfinden.

Pos.Nr	Menge ME	Bild	Artikelnummer Artikelbezeichnung	Richtpreis exkl. MwSt	Total exkl. MwSt
30	1 ST		2116 811.105.000 Waschtisch Alterna moderna 60 x 45 cm, Armaturenloch mit Überlauf Befestigungsmaterial weiss Cleaneffekt	195.00	195.00

Viele Grossisten bieten Ihnen Apps und Onlineprogramme an, um entsprechende Apparatemasse herauszufinden. In der Regel kriegen Sie diese aber auch von Ihrem Projektleiter oder Vorgesetzten.

Auftrag 2

Auf der Baustelle sollten Sie die wichtigsten Masse und Eckdaten der Standartapparate wissen. Um diese Masse zu lernen, zeichnen Sie nun die wichtigsten sechs Details im Massstab 1:10 auf. Unter nachfolgendem Button finden Sie entsprechende leere Planvorlagen.

[Link zum Dokument](#)

Über nebenstehenden Link finden Sie leere Planvorlagen im Format A4 und im Format A3.

Tipp: Für die Standartübungen 3-7 sollte ein A4 Plan reichen!



3. Waschtisch inkl. Spiegelschrank

- a) Zeichnen Sie die Ansicht des Waschtischs inkl. Spiegelschrank im Massstab 1:10 auf.
b) Vermessen Sie alle für die Roh- und Fertigmontage wichtigen Punkte.

Technische Daten


Waschtisch:	Breite: 60cm	Höhe: 20cm	Schraubenabstand: 28cm
Spiegelschrank:	Breite 60cm	Höhe: 80cm	
Unterlagsboden:	Höhe: 10cm		

4. Wandklosett UP

- a) Zeichnen Sie die Ansicht der WC Anlage inkl. UP Spülkasten im Massstab 1:10 auf.
b) Vermessen Sie alle für die Roh- und Fertigmontage wichtigen Punkte.

Technische Daten

Wand-Klosett:	Breite: 40cm
Unterlagsboden:	Höhe: 12.5cm

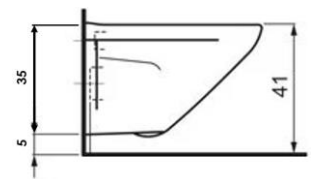**5. Dusche AP**

- a) Zeichnen Sie die Ansicht der Dusche inkl. mech. AP Mischer im Massstab 1:10 auf.
b) Vermessen Sie alle für die Roh- und Fertigmontage wichtigen Punkte.

Technische Daten

Dusche:	Breite: 100cm
Duschgleitstange:	Länge 110cm
Unterlagsboden:	Höhe: 10cm

6. Badewanne UP

- a) Zeichnen Sie die Ansicht der Badewanne inkl. mech. UP Mischer im Massstab 1:10 auf.
b) Vermessen Sie alle für die Roh- und Fertigmontage wichtigen Punkte.

Technische Daten

Wanne:	Breite: 160cm	Höhe: 55cm	
Armatur:	Position: Mitte	Auslauf Brause:	rechts
Unterlagsboden:	Höhe: 7.5cm		

7. Küche

- a) Zeichnen Sie die Ansicht der Küche inkl. mech. Einhebelmischer im Massstab 1:10 auf.
b) Vermessen Sie alle für die Roh- und Fertigmontage wichtigen Punkte.

Technische Daten

Unterlagsboden:	Höhe: 10 cm
-----------------	-------------

Auftrag 3



Auf der Baustelle kommt ein Apparat selten allein vor. In der Regel müssen Sie eine komplette Nasszelle wie unten installieren. Erstellen Sie einen Rohbauplan für die bevorstehende Rohmontage.

8. Nasszelle

- Zeichnen Sie die Ansicht der nachfolgenden vier Apparate im Massstab 1:10 auf.
- Vermessen Sie alle für die Rohmontage wichtigen Punkte.

Technische Daten

Wanne:	Breite: 70cm	Länge: 170cm
Wand-Klosett:	Breite: 40cm	Höhe: 35cm
Waschtisch:	siehe Skizze	
Dusche:	Standartinstallation mit Armatur AP rechts der Mitte	
Unterlagsboden:	Höhe: 10cm	

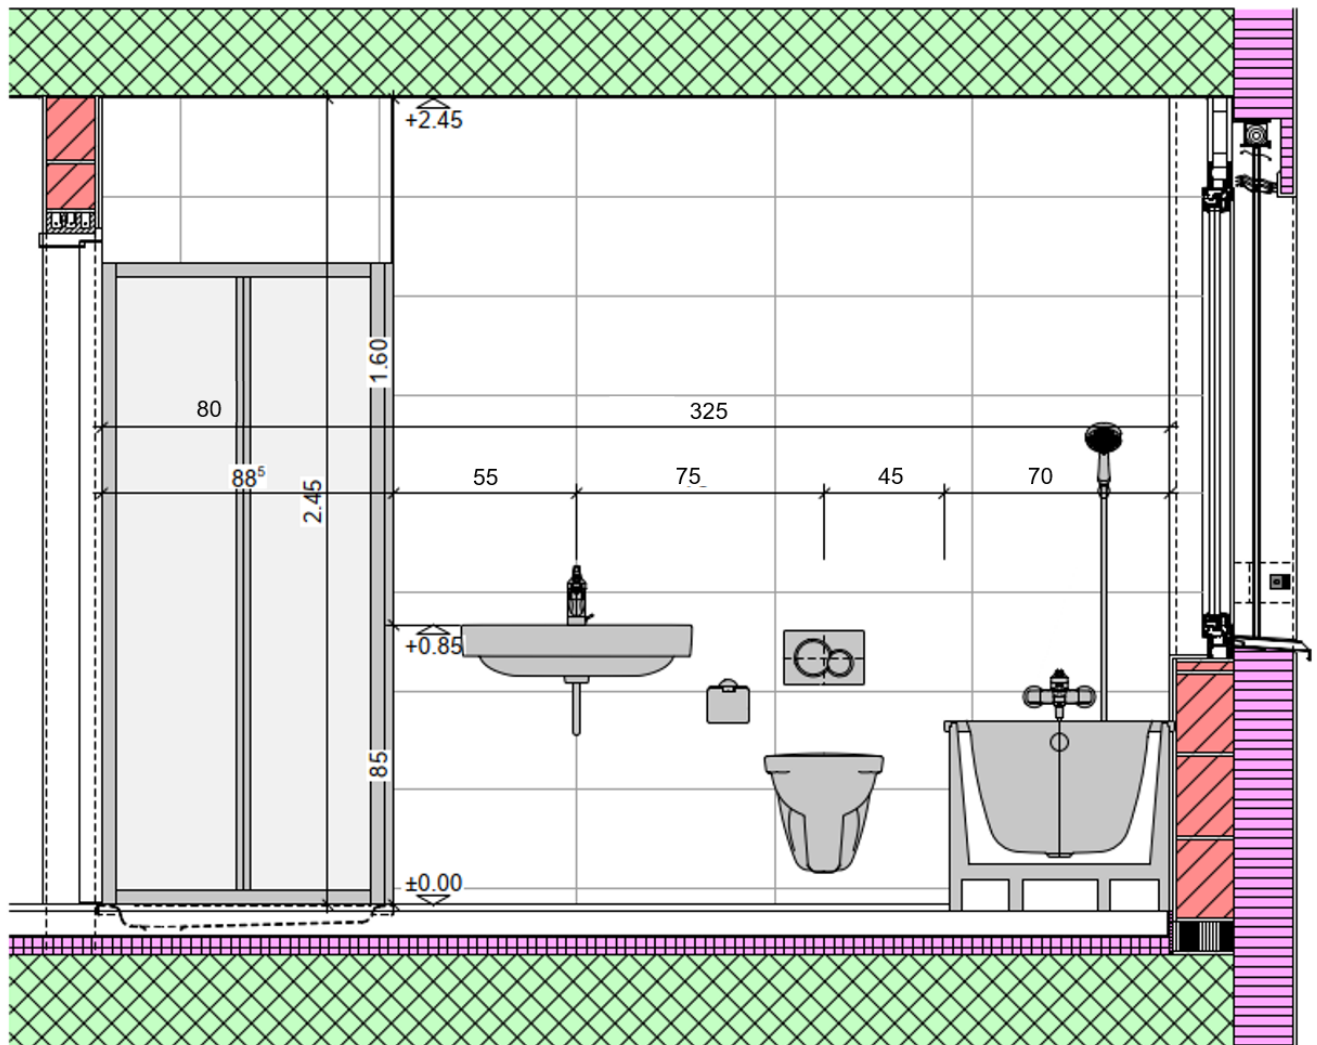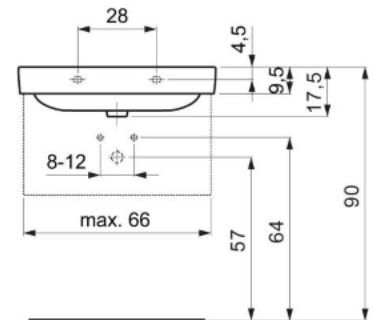

9. Separat WC

Sie erhalten von Ihrem Chefmonteure den Auftrag, ein separates WC inkl. Waschtisch und Spiegel zu installieren. Dazu erhalten Sie untenstehenden Architekturpläne. Erstellen Sie einen Rohbauplan für die bevorstehende Rohmontage. Die technischen Daten entnehmen Sie bitte der Apparateliste des Lieferanten.



- Zeichnen Sie die Ansicht der Apparate im Massstab 1:10 in einer A4 Vorlage auf.
- Vermessen Sie alle für die Rohmontage wichtigen Punkte.
- Unterlagsboden: Höhe: 10cm

[Link zum Dokument](#)

Über nebenstehenden Link finden Sie die Apparateliste der Aufgabe.



Architekturplan

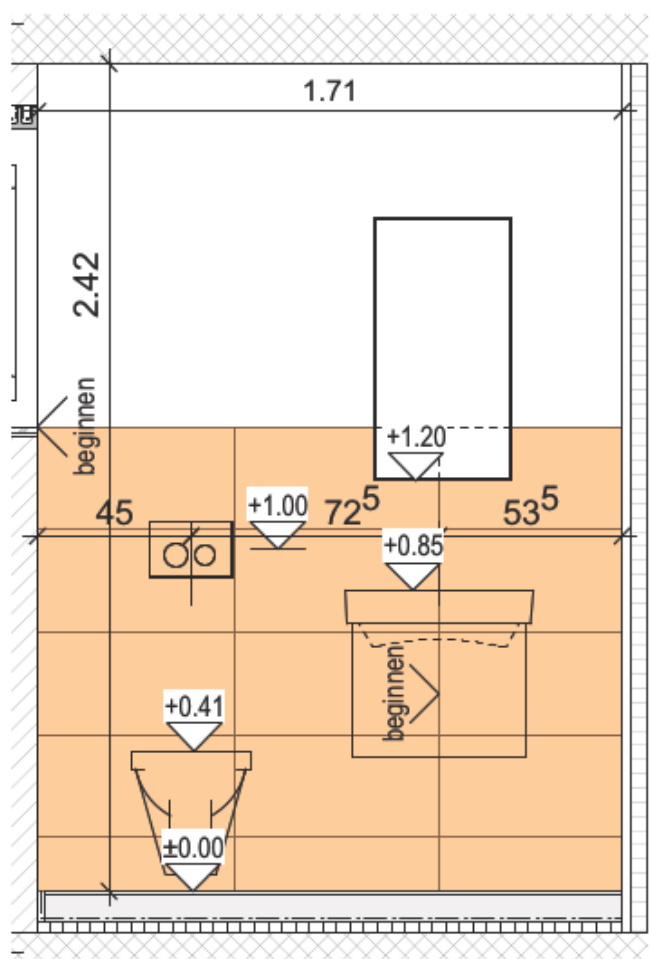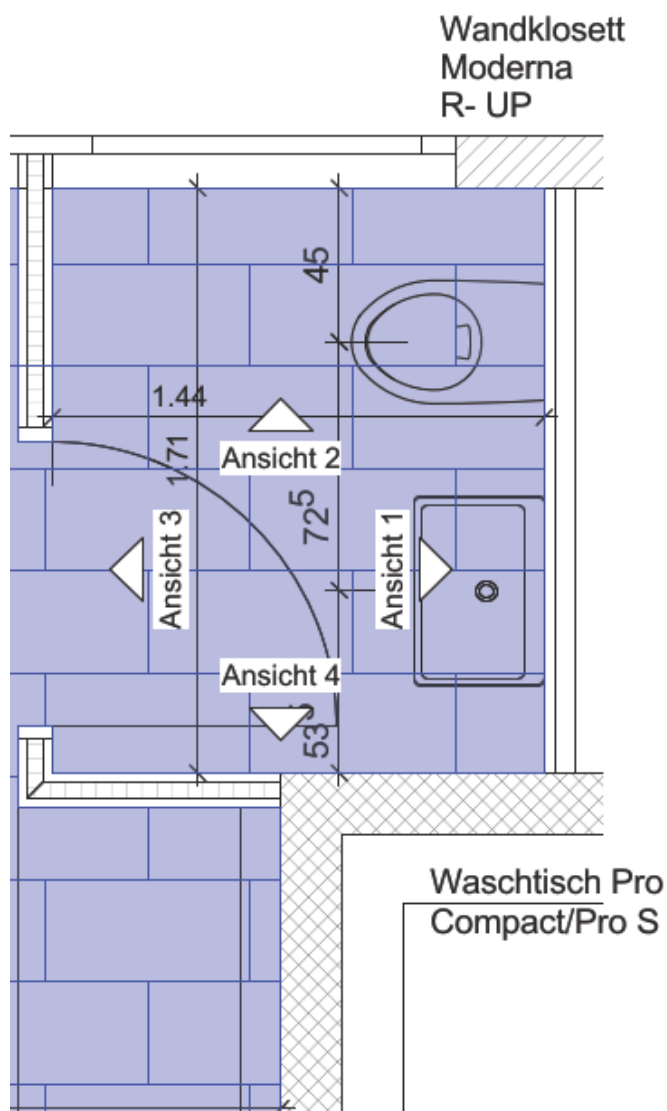

10. WT / BW

Sie erhalten von Ihrem Chefmonteure den Auftrag, ein separates WC inkl. Waschtisch und Spiegel zu installieren. Dazu erhalten Sie untenstehenden Architekturpläne. Erstellen Sie einen Rohbauplan für die bevorstehende Rohmontage. Die technischen Daten entnehmen Sie bitte der Apparateliste des Lieferanten.


- Zeichnen Sie die Ansicht der Apparate im Massstab 1:10 in einer A3 Vorlage auf.
- Vermessen Sie alle für die Rohmontage wichtigen Punkte.
- Unterlagsboden: Höhe: 15cm

Link zum Dokument

Über nebenstehenden Link finden Sie die Apparateliste der Aufgabe.



Architekturplan

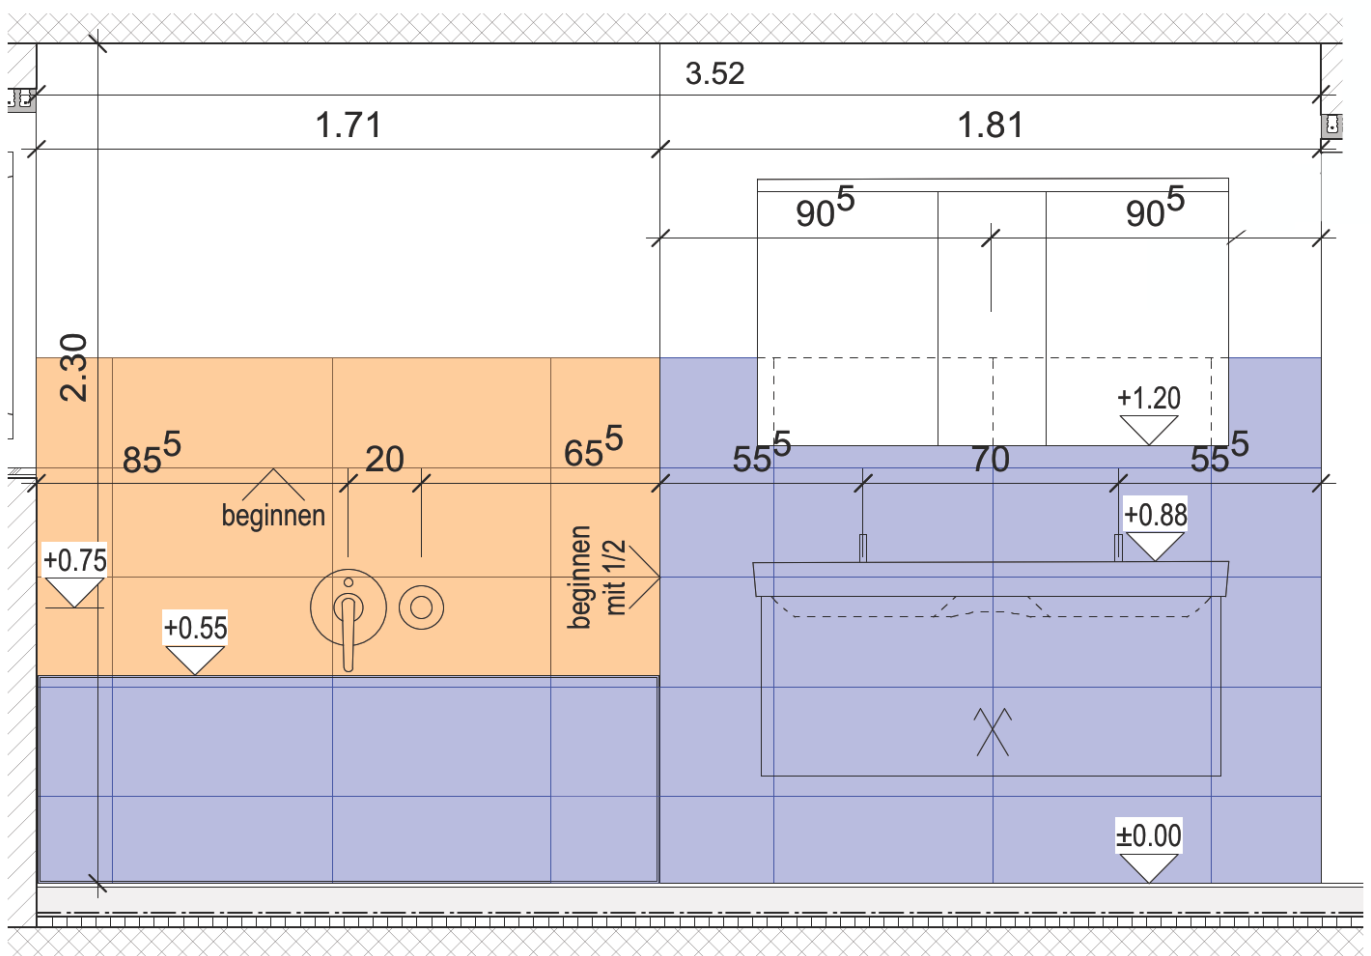

11. WT / DU

Sie erhalten von Ihrem Chefmonteuer den Auftrag, einen Waschtisch inkl. Spiegelschrank und Dusche zu installieren. Dazu erhalten Sie untenstehenden Architekturpläne. Erstellen Sie einen Rohbauplan für die bevorstehende Rohmontage. Die technischen Daten entnehmen Sie bitte der Apparateliste des Lieferanten.


- Zeichnen Sie die Ansicht der Apparate im Massstab 1:10 in einer A3 Vorlage auf.
- Vermessen Sie alle für die Rohmontage wichtigen Punkte.
- Unterlagsboden: Höhe: 13cm

Link zum Dokument

Über nebenstehenden Link finden Sie die Apparateliste der Aufgabe.



Architekturplan

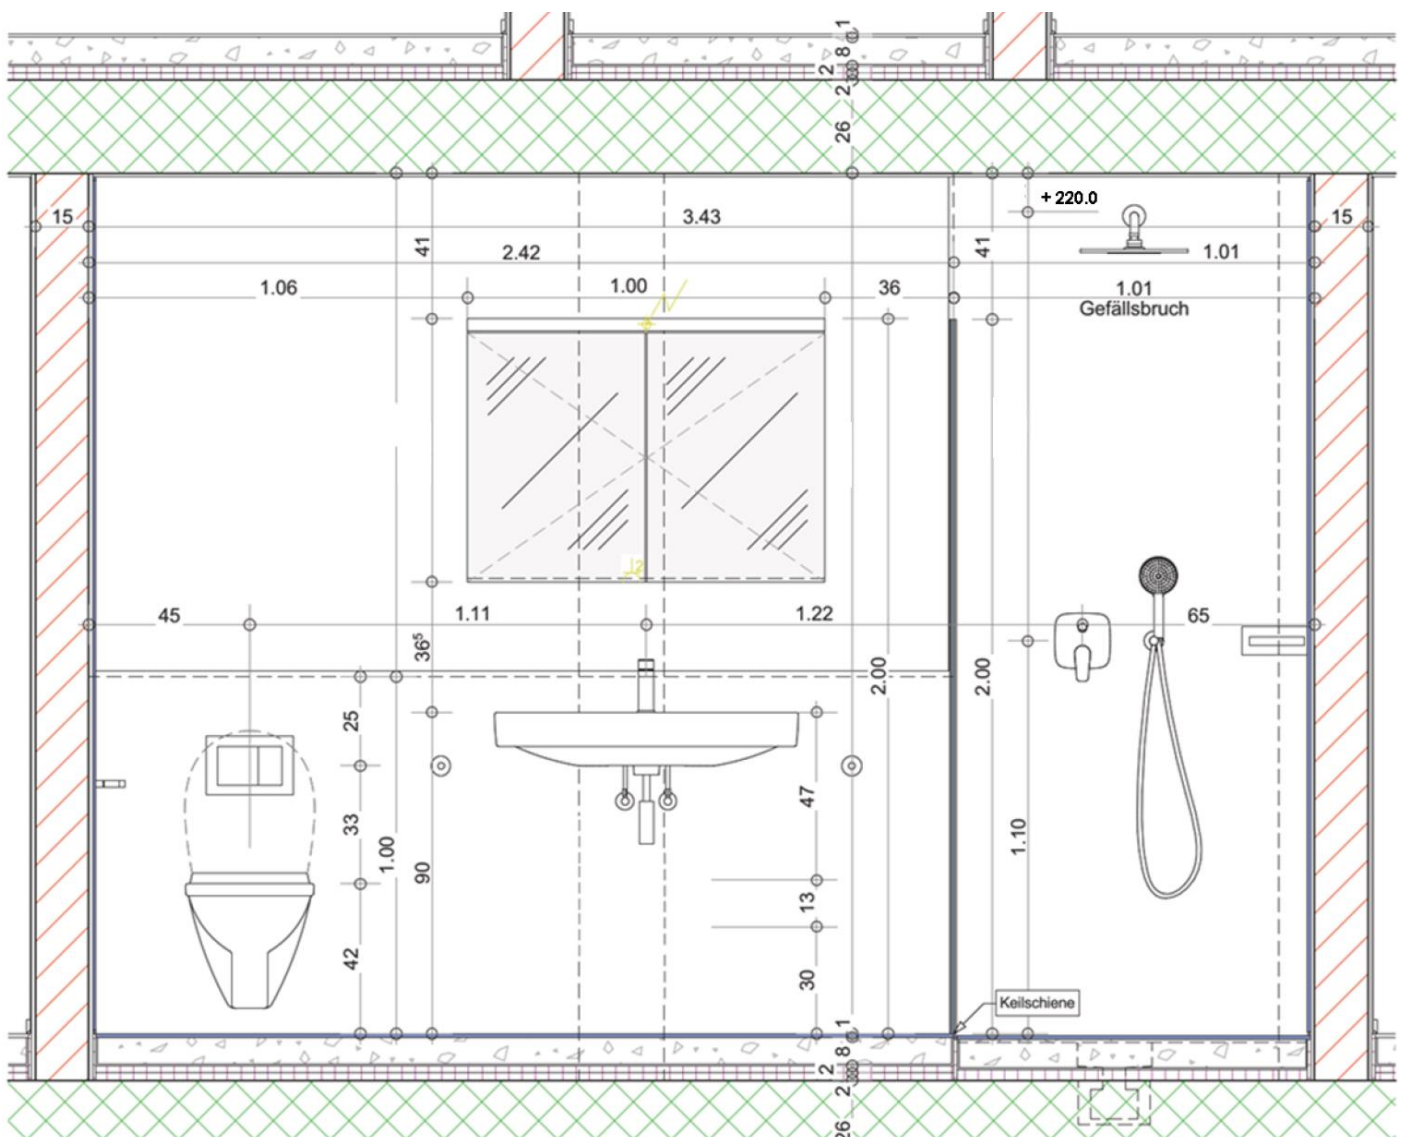

Auftrag 6 - Leistungsnachweis

Als Leistungsnachweis erstellen eine Detailplanung unserer Nasszelle im Herren WC im 2.Obergeschoss unseres Schulhauses. Alle relevanten Daten und Details zu dieser Aufgabe entnehmen Sie bitte aus der A3 Aufgabe. Eine leere A3 Planvorlage für Ihre Arbeit finden Sie via untenstehendem Link.

Leistungsnachweis zum Thema Planen und Einteilen von Apparaten

Beschriften Sie den Plankopf mit dem Titel «Leistungsnachweis 3.1»



Link zu einer leeren Planvorlage

Über nebenstehenden Link finden Sie leere Planvorlagen im Format A3.



Abgabe des Lernprodukts in Teams

- Ich habe das Lernprodukt erstellt und abgelegt für die spätere Abgabe

