

Detailplan erstellen

Name:

Datum:

Lernziele Modul

- Sie bestimmen anhand von Beispielen den Platzbedarf, Achsabstände und Montagehöhen von Apparaten und den zugehörigen Garnituren. Ja ☐ Nein ☐
- Sie erstellen anhand von Planunterlagen einen Werkstattplan für eine Vorwand. Ja ☐ Nein ☐

Lernprodukte

- Leistungsnachweis «Detailplanung Badezimmer» ☐

Situation

Im vierten Semester haben Sie gelernt Apparate selbständig zu platzieren und daraus einen Detailplan zu erstellen. Diese Fertigkeiten möchten wir nun verfeinern und unseren Fokus auf die Erstellung des Detailplanes zu legen. Wir lernen dabei das Zeichnen auf komplett weissen Blättern und wie man eine korrekte Strahlvermassung erstellt. Im Anschluss planen Sie die komplette Vorwand inkl. Materialauszug damit Sie die Installation auf der Baustelle vornehmen können.


Achten Sie darauf sehr sauber und genau zu zeichnen, Detailpläne müssen exakt und verständlich sein!



Auftrag 1

In diesem Auftrag möchten wir zuerst die Strahlvermassung lernen und einmal gemeinsam erstellen. Die Strahlvermassung ist eine Technik, die es uns erlaubt sauber und gleichmässig zu vermessen.

1. Erstellen Sie die Detailplanung eines «Standard Waschtisches» inkl. Achs- und Strahlvermassung.

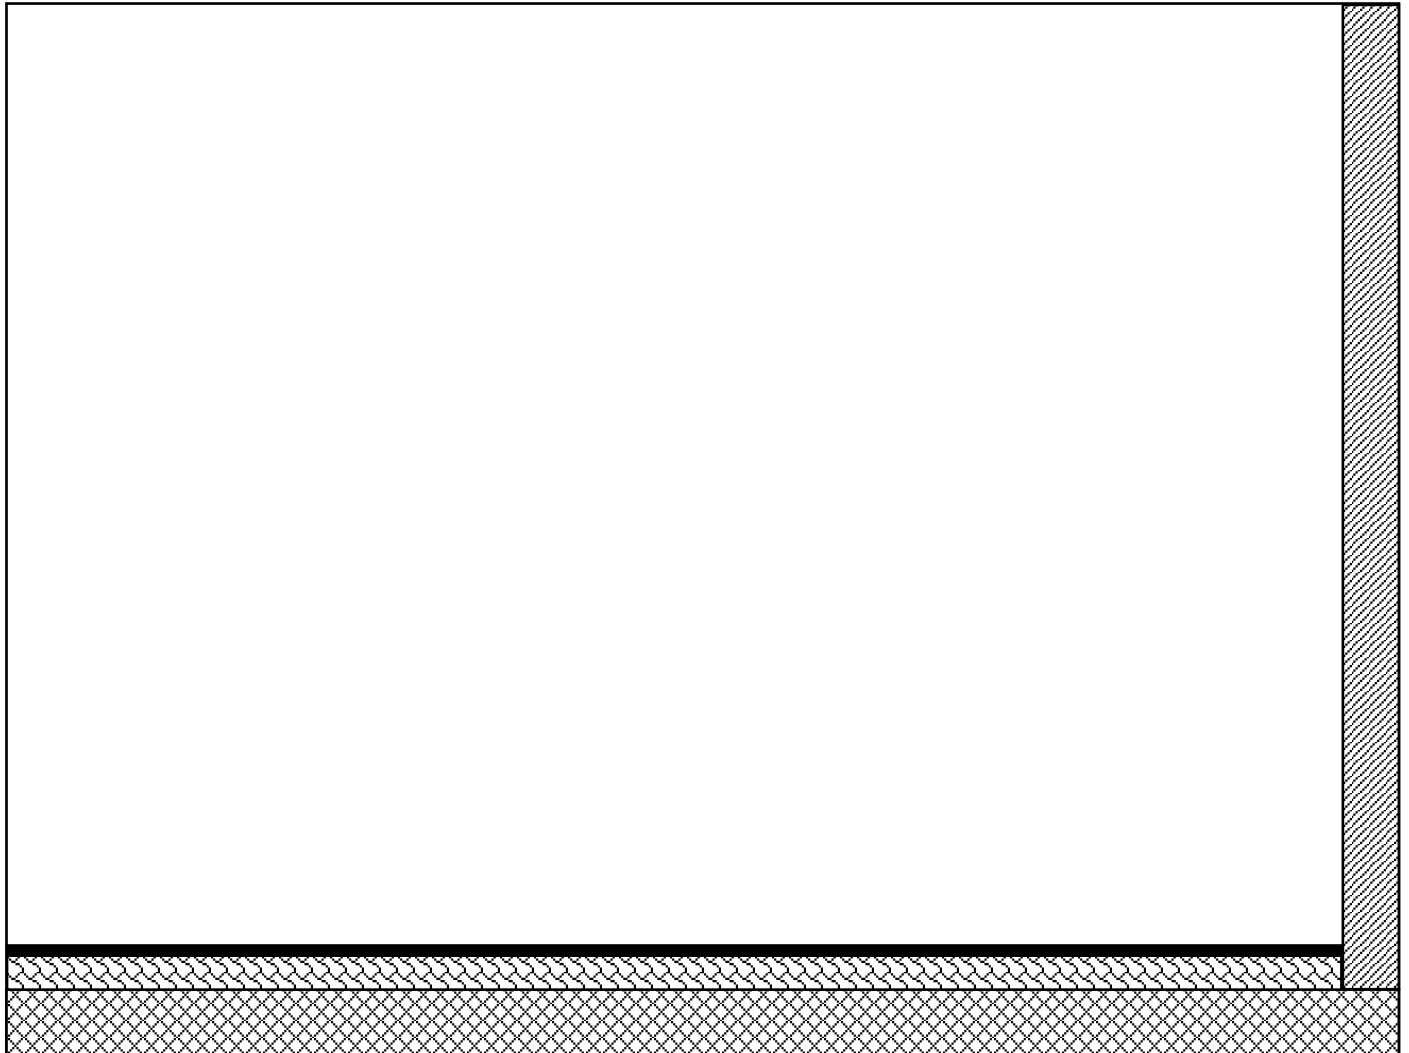

Wichtige Hinweise / Details / Notizen



Link zum Dokument

Über nebenstehenden Link finden Sie leere Planvorlagen im Format A3.



A3 Plan leer

2. Aufgabe Nasszelle WHG 2 WC / BAD

- a) Erstellen Sie die Detailplanung im Massstab 1:10
- b) Vermessen Sie die für die Vorwandmontage relevanten Punkte mit einer Strahlvermessung.
⇒ Vermessen Sie auf den fertigen Boden / unabhängig vom Unterlagsboden.
- c) Erstellen Sie die Vorwandplanung mit Geberit Duofix inkl. Materialauszug.

Nasszelle WHG 2 WC / BAD

Über den Link finden Sie komplette Aufgabe inkl. Detailskizzen.



Planvorlage A3

Überprüfen Sie Ihre Resultate

Überprüfen Sie selbstständig ihre Resultate unter folgendem Link.



Lösungen

3. Aufgabe Nasszelle WHG 2 WC / DU

- c) Erstellen Sie die Detailplanung im Massstab 1:10
- d) Vermessen Sie die für die Vorwandmontage relevanten Punkte mit einer Strahlvermessung.
⇒ Vermessen Sie auf den fertigen Boden / unabhängig vom Unterlagsboden.
- c) Erstellen Sie die Vorwandplanung mit Geberit GLS inkl. Materialauszug.

Nasszelle WHG 2 WC / BAD

Über den Link finden Sie komplette Aufgabe inkl. Detailskizzen.



Planvorlage A3

Überprüfen Sie Ihre Resultate

Überprüfen Sie selbstständig ihre Resultate unter folgendem Link.



Lösungen

4. Aufgabe Nasszelle WC / DU 2 WHG 2, EG

- e) Erstellen Sie die Detailplanung im Massstab 1:10
- f) Vermessen Sie die für die Vorwandmontage relevanten Punkte mit einer Strahlvermessung.
⇒ Vermessen Sie auf den fertigen Boden / unabhängig vom Unterlagsboden.
- c) Erstellen Sie die Vorwandplanung inkl. Materialauszug.

Hinweis: Es sind zwei Vorwände, die in der Ecke verbunden werden müssen!

Nasszelle WC / DU 2 WHG 2, EG

Über den Link finden Sie komplette Aufgabe inkl. Detailskizzen.



Planvorlage A3

Überprüfen Sie Ihre Resultate

Überprüfen Sie selbstständig ihre Resultate unter folgendem Link.



Lösungen

5. Aufgabe Nasszelle DU Gäste WHG 5, AT

- g) Erstellen Sie die Detailplanung im Massstab 1:10
- h) Vermessen Sie die für die Vorwandmontage relevanten Punkte mit einer Strahlvermessung.
⇒ Vermessen Sie auf den fertigen Boden / unabhängig vom Unterlagsboden.
- c) Erstellen Sie die Vorwandplanung inkl. Materialauszug.

Nasszelle DU Gäste WHG 5, AT

Über den Link finden Sie komplette Aufgabe inkl. Detailskizzen.



Planvorlage A3

Überprüfen Sie Ihre Resultate

Überprüfen Sie selbstständig ihre Resultate unter folgendem Link.



Lösungen

Auftrag 3 - Leistungsnachweis

Als Leistungsnachweis erstellen Sie eine exakte Detailplanung der unten angegebenen Situation.

Aufgabe Leistungsnachweis

- i) Erstellen Sie die Detailplanung im Massstab 1:10
- j) Vermessen Sie die für die Vorwandmontage relevanten Punkte mit einer Strahlvermessung.
⇒ Vermessen Sie auf den fertigen Boden / unabhängig vom Unterlagsboden.
- c) Erstellen Sie die Vorwandplanung mit Geberit GIS inkl. Materialauszug.

Leistungsnachweis zum Thema Planen und Einteilen von Apparaten

Via nebenstehenden Link finden Sie die Aufgabe «Leistungsnachweis»



Abgabe des Lernprodukts in Teams

- Ich habe das Lernprodukt erstellt und abgelegt für die spätere Abgabe

